


ОФИС ПРОДАЖ 40 × 12 м — ПЛАН 1-ГО ЭТАЖА (отм. 0.000)

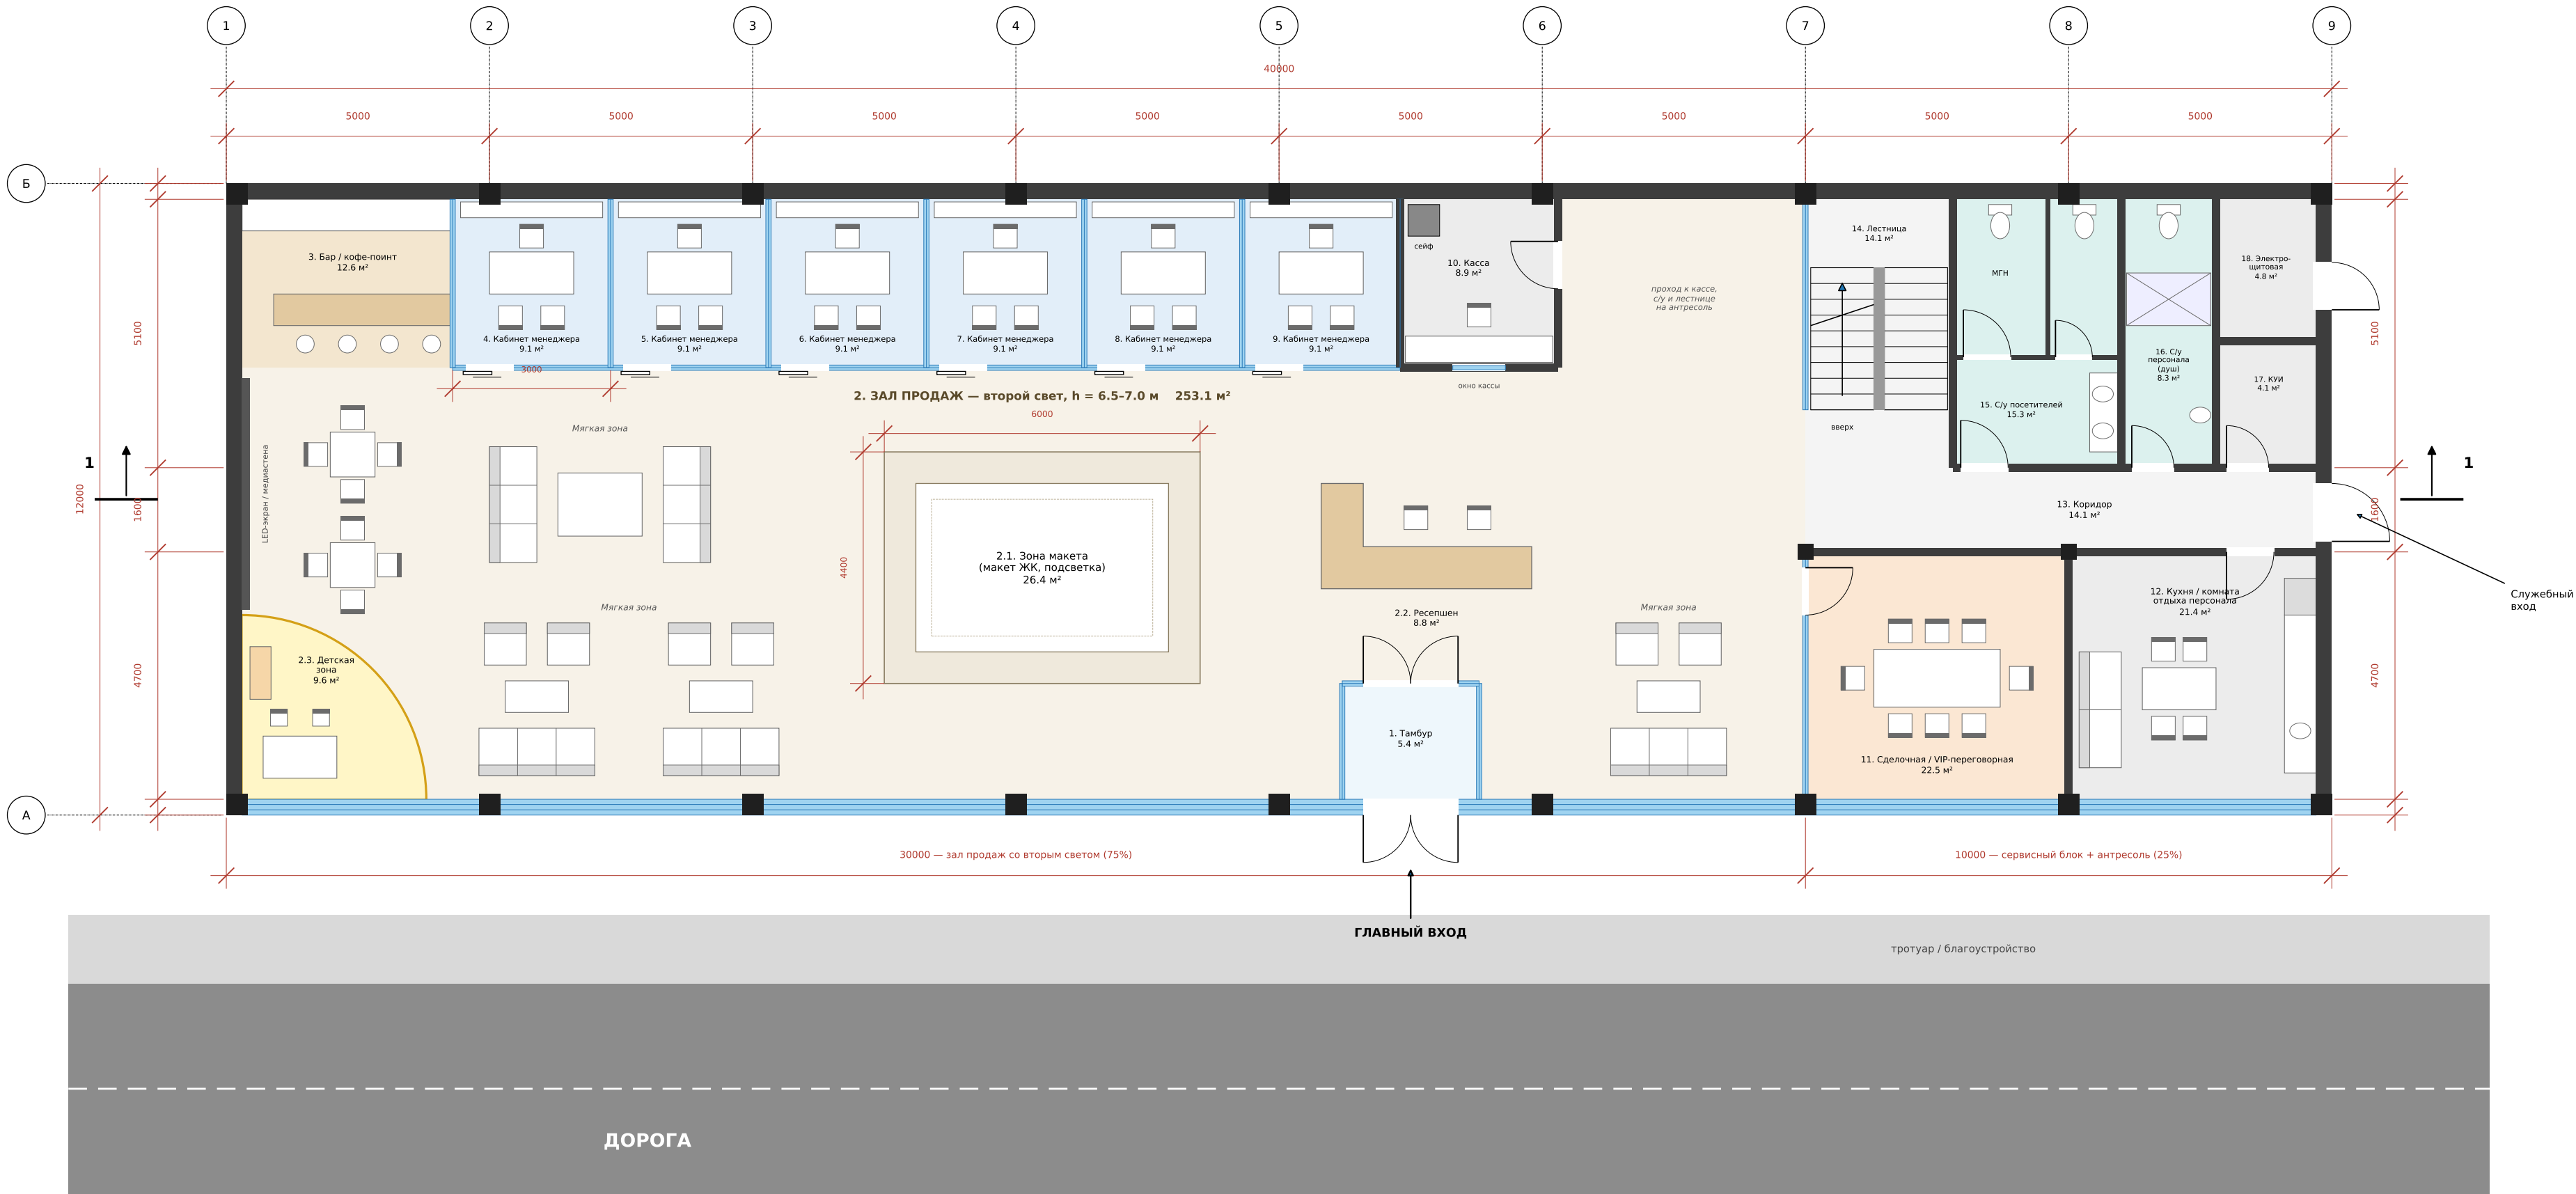

Экспликация помещений 1-го этажа		
№	Наименование	Площадь, м²
1	Тамбур	5.4
2	Зал продаж (второй свет h 6.5–7.0 м), в т.ч.:	253.1
2.1	зона макета	26.4
2.2	ресепшен	8.8
2.3	детская зона	9.6
	мягкие зоны (4 шт.)	—
3	Бар / кофе-пойнт	12.6
4–9	Кабинеты менеджеров, 6 шт. × 9.1	54.6
10	Касса	8.9
11	Сделочная / VIP-переговорная	22.5
12	Кухня / комната отдыха персонала	21.4
13	Коридор	14.1
14	Лестница на антресоль	14.1
15	С/у посетителей (в т.ч. МГН)	15.3
16	С/у персонала с душем	8.3
17	КУИ (уборочный инвентарь)	4.1
18	Электрощитовая	4.8
ИТОГО 1-й этаж (полезная)		439.2

Примечания


- Здание 40.0 × 12.0 м по наружным граням, площадь застройки 480 м². Витражный фасад — вдоль дороги.
- Зал продаж 30 × 12 м — двухсветное пространство высотой 6.5–7.0 м (75% площади).
- Сервисный блок 10 × 12 м (25%): под антресолью h = 3.0 м, над ним антресоль бэк-офиса на отм. +3.300, h = 3.7 м (см. лист 2).
- Кабинеты менеджеров — стеклянные перегородки h = 3.0 м, раздвижные двери; над кабинетами на задней стене — место под брендинг / медиаэкран (отм. +3.5...+6.0).
- Шаг колонн 5.0 м, пролёт 12 м без промежуточных опор (уточняется расчётом КР).
- Наполнение взято из исходного проекта: бар, ресепшен, детская зона, зона макета, кабинеты менеджеров, касса, кухня, комната отдыха, санузлы, лестница, переговорные.
- Эвакуационные выходы, МГН, вентиляция и инженерные сети — уточнить на стадии «П».

Условные обозначения

- Клиентская зона (второй свет)
- Кабинеты менеджеров
- Переговорные с клиентами
- Бэк-офис
- Служебные помещения
- Санузлы
- Наружная стена
- Витраж / стеклянная перегородка
- Колонна
- Перегородка

Офис продаж 40 × 12 м с антресолью (бэк-офис)		
Эскизная планировка. Функциональное наполнение — по ТЗ заказчика		
План 1-го этажа	Стадия	Лист
Масштаб 1:100 (формат A2)	ЭП	1

ОФИС ПРОДАЖ 40 × 12 м — ПЛАН АНТРЕСОЛИ (отм. +3.300) И РАЗРЕЗ 1-1

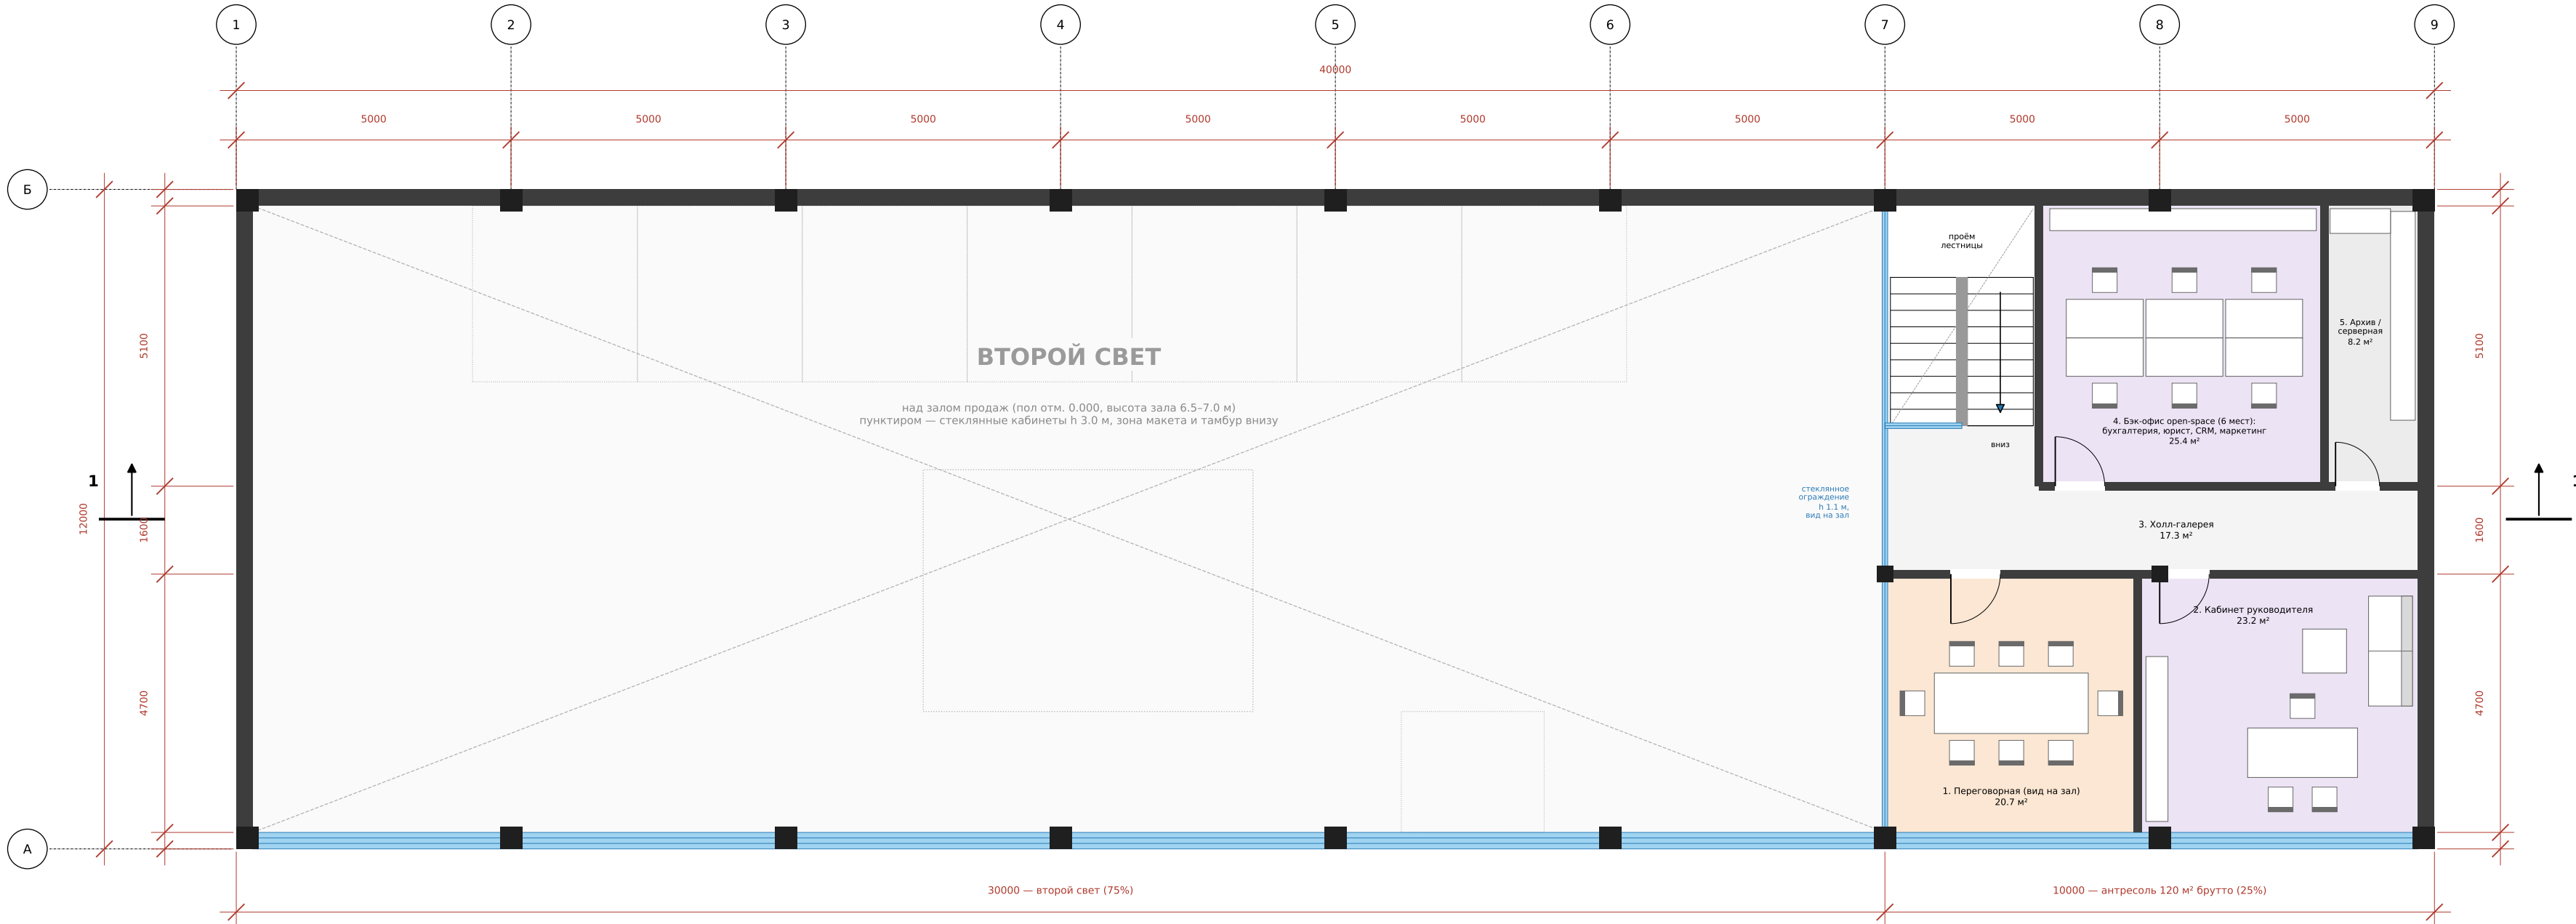

Экспликация антресоли (отм. +3.300)		
№	Наименование	Площадь, м²
1	Переговорная (стекло на зал)	20.7
2	Кабинет руководителя	23.2
3	Холл-галерея с видом на зал	17.3
4	Бэк-офис орел-спрае, 6 мест	25.4
5	Архив / серверная	8.2
	Проём лестницы	10.9
ИТОГО антресоль (полезная)		94.8
Антресоль brutto / доля от 480 м²		120 / 25%

Примечания


- Антресоль 10 × 12 м = 120 м² brutto (25% от 480 м²), полезная 94.8 м² (≈20%).
- Отм. пола антресоли +3.300; высота помещений антресоли 3.7 м (до низа покрытия +7.000).
- Край антресоли по оси 7 — стеклянное ограждение h 1.1 м и стеклянная стена переговорной: бэк-офис и переговорная получают вид на зал и макет.
- Лестница двухмаршевая, 2 × 10 подъёмов (165 × 300 мм), ширина марша 1.2 м.
- Колонны антресоли — по осям 7 и 8 (сечения и перекрытие — по расчёту КР).

Условные обозначения

- Клиентская зона (второй свет)
- Кабинеты менеджеров
- Переговорные с клиентами
- Бэк-офис
- Служебные помещения
- Санузлы

- Наружная стена
- Витраж / стеклянная перегородка
- Колонна
- Перегородка

Разрез 1-1

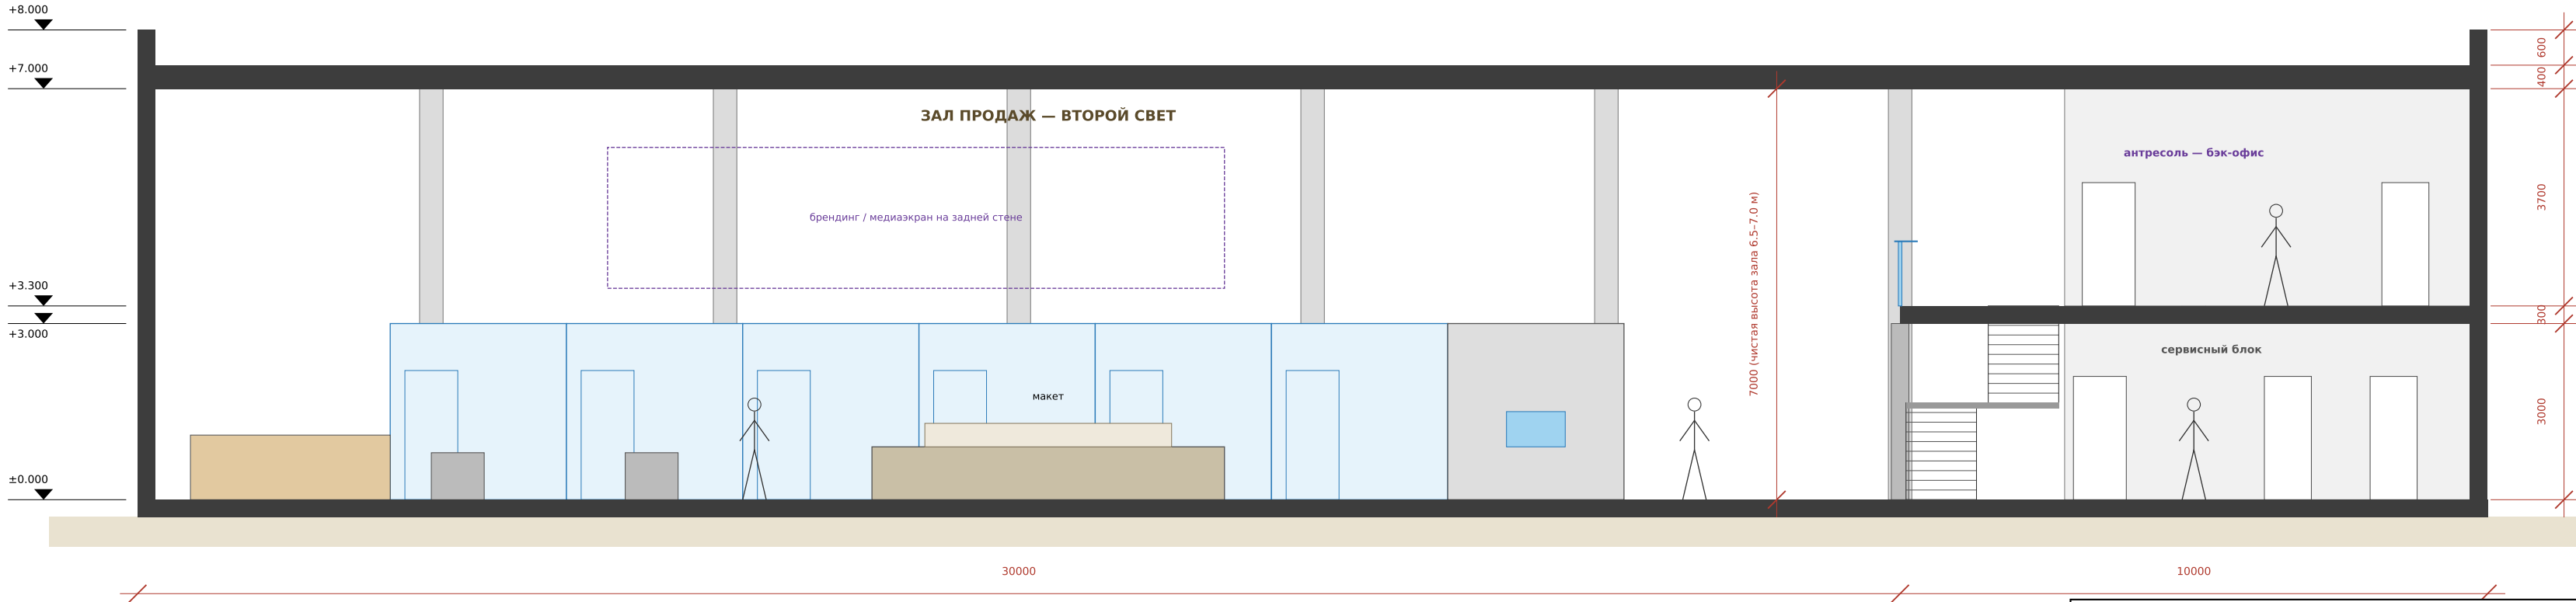

Офис продаж 40 × 12 м с антресолью (бэк-офис)		
Эскизная планировка. Функциональное наполнение — по ТЗ заказчика		
План антресоли (бэк-офис), разрез 1-1	Стадия	Лист
Масштаб 1:100 (формат А2)	ЭП	2